

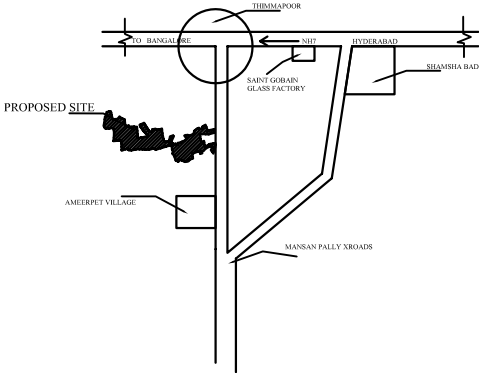
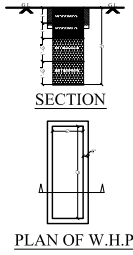
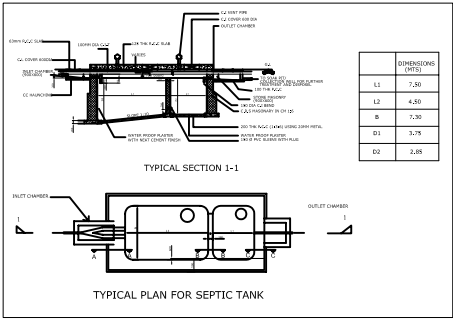
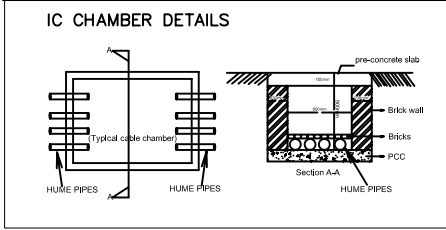


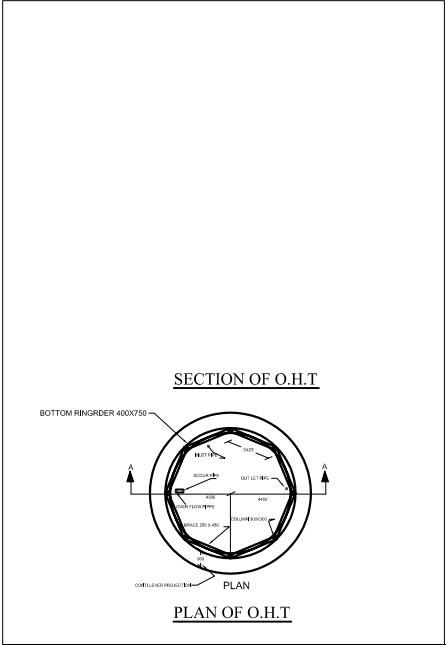

LOCATION PLAN

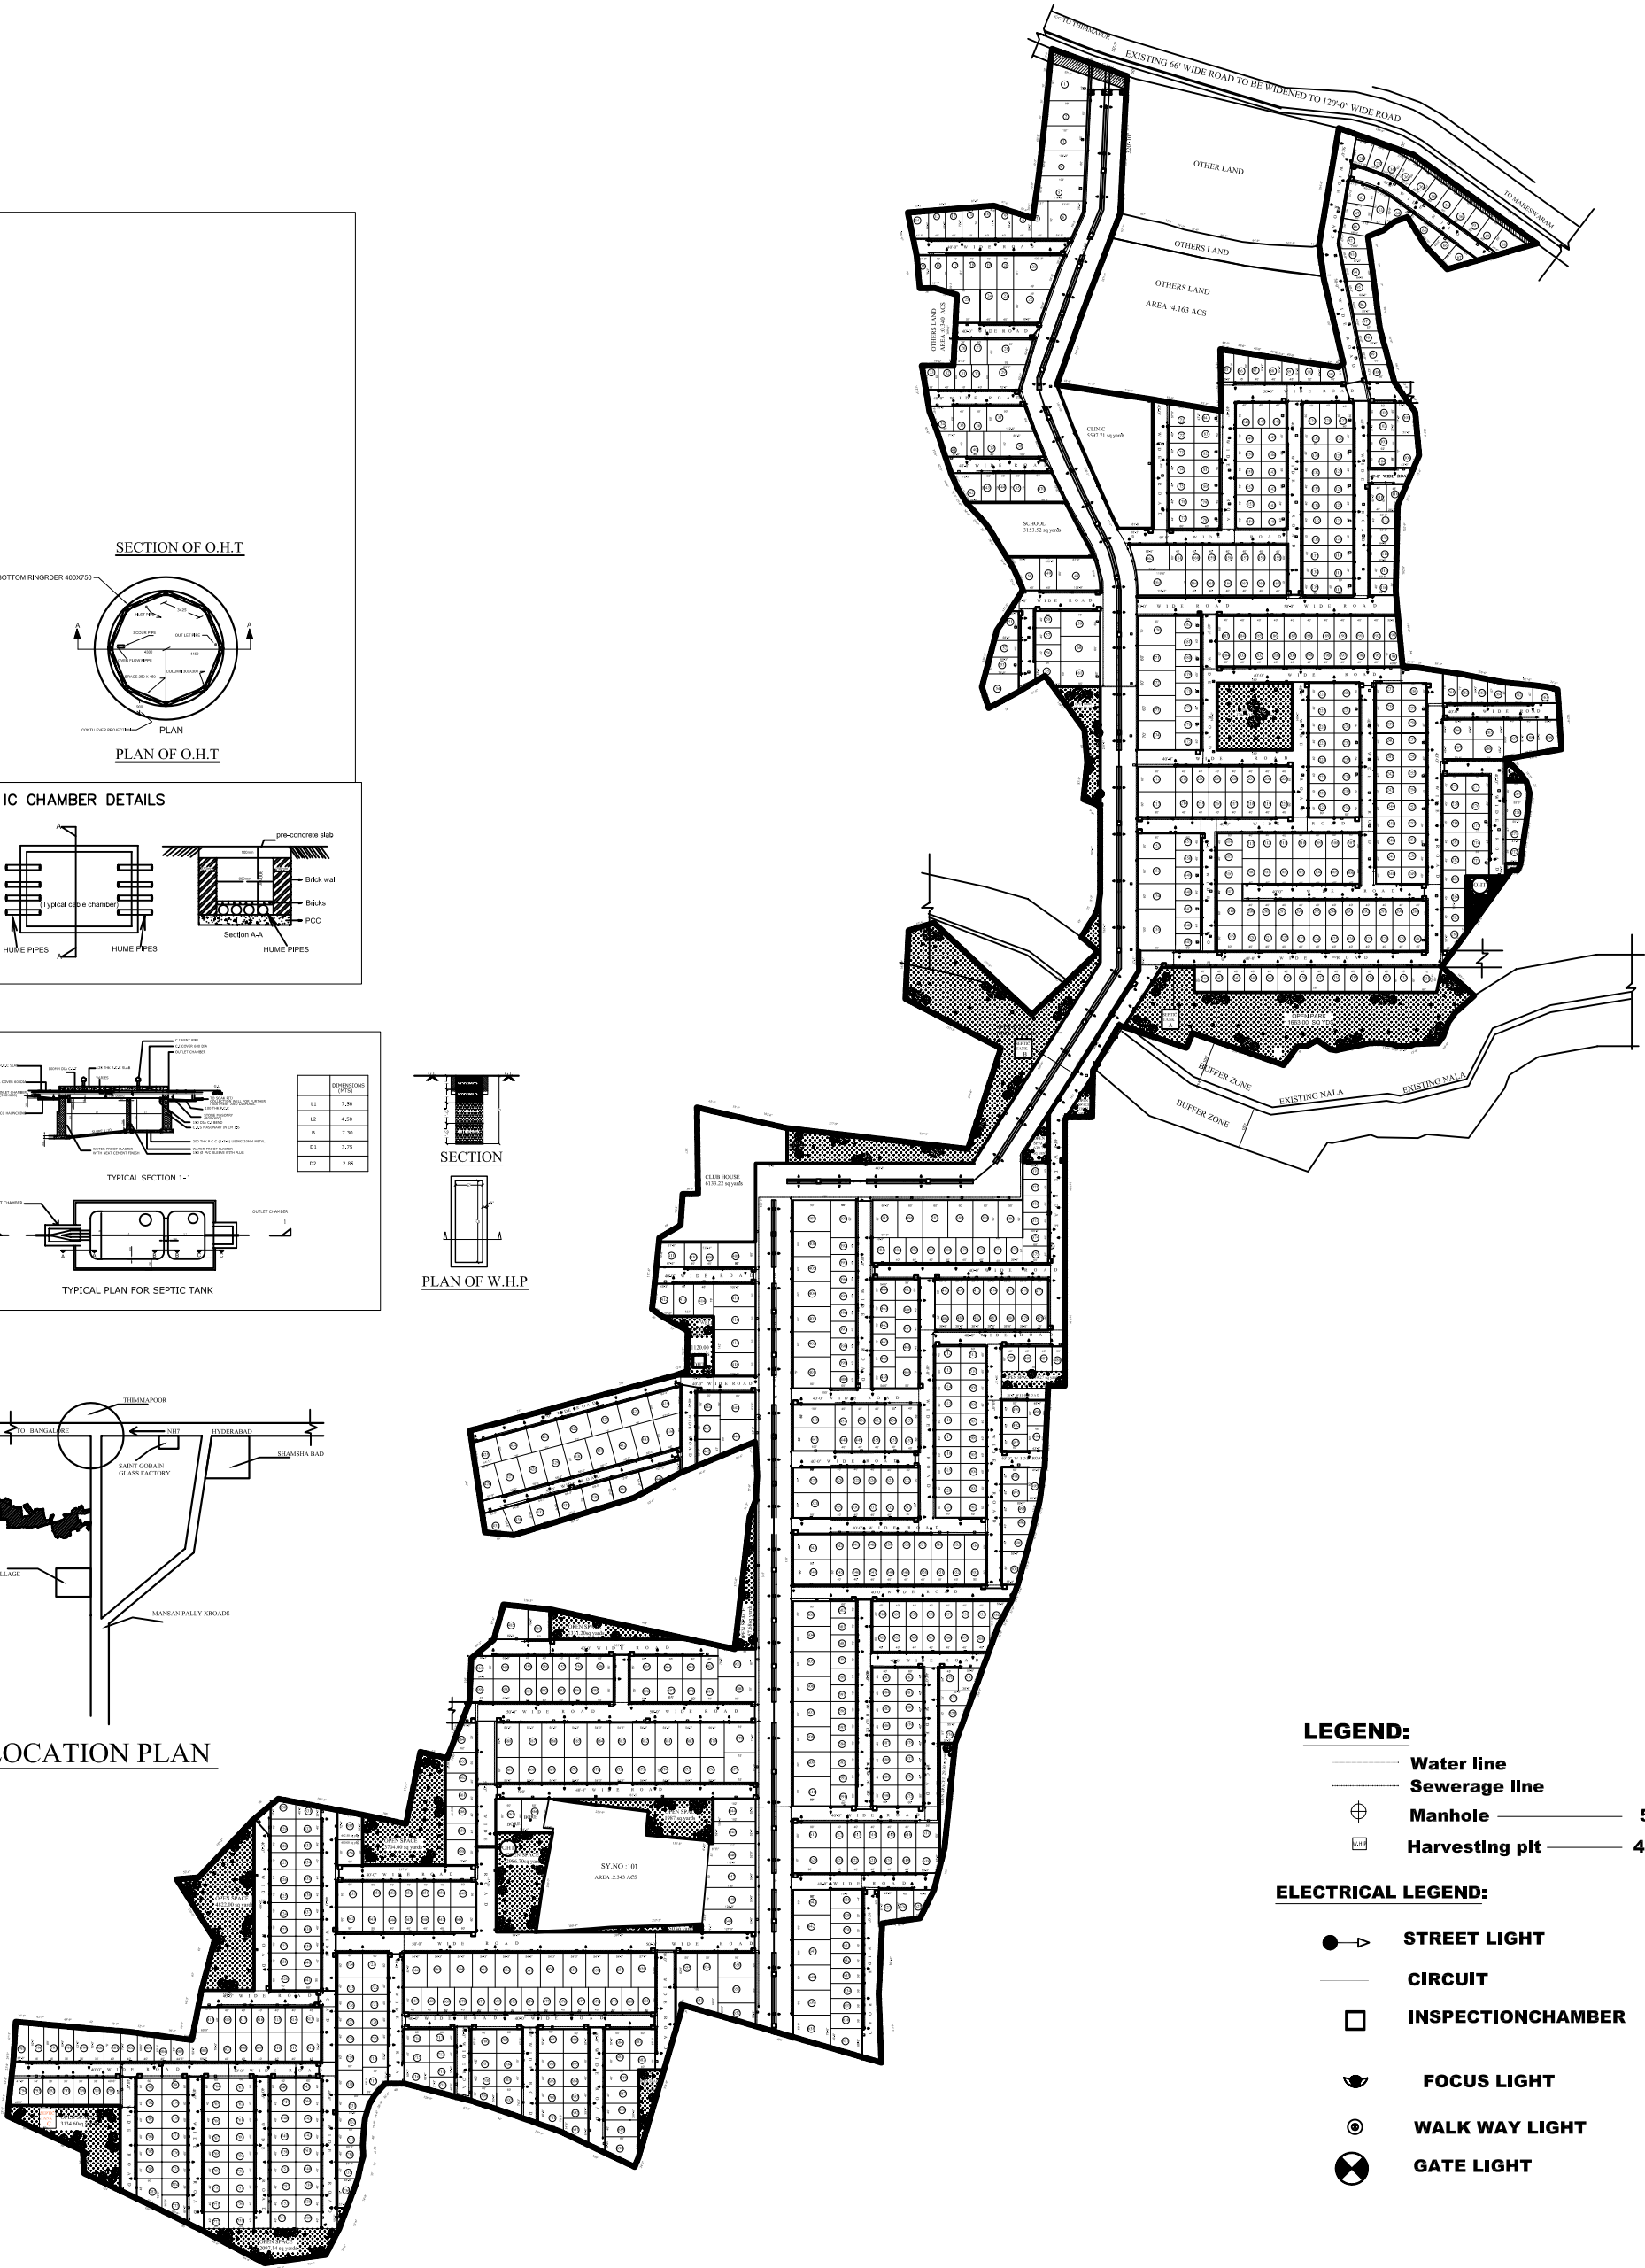

LEGEND:

- Water line
- Sewerage line
- Manhole 570 no's
- Harvesting pit 400 no's

ELECTRICAL LEGEND:

- STREET LIGHT
- CIRCUIT
- INSPECTION CHAMBER
- FOCUS LIGHT
- WALK WAY LIGHT
- GATE LIGHT 4 no's

PLAN SHOWING THE FINAL LAY-OUT PLAN BEARING SURVEY NO'S: 62,74,75,76,77,88,95,96,98,99,100,101,102,103,109,110,111,112, 113,114,115,118,215,231,232,233,234,235,236,237,238,239,241,242,243, 245,246,247,248,249,250,251,252,253,254,262,263,264,279,280,281, 283,284,286,287,288, OF AMIEERPET VILLAGE & TUPRA KHURDU VILLAGE ,AT MAHESWARAM MANDAL, R R DISTRICT. BELONGING TO

- KARVY REALTY & SERVICES (INDIA) LTD,
- BLUE PLANET HOUSING & INFRASTRUCTURE PVT LTD,
- HEARTLAND INFRASTRUCTURE PVT LTD,
- METEOR INFRASTRUCTURE & PROJECTS PVT LTD.


REPRESENTED BY
SRI G. SRIDHAR

- REFERENCE:
- LAYOUT BOUNDARY
 - TOTAL LAYOUT AREA : 556660.55 SQYDS (OR) (115 ACRES 0.5 GUNTAS)
 - TOTAL NO PLOTS : 906 Nos.
 - WHP : 400 NO'S

LAND USE ANALYSIS	IN SQ.YDS	PERCENTAGE
PLOTTED AREA	304953.91	54.782%
AMENITIES AREA	14884.45	2.674 %
OPEN AREA	55666.83	10.000 %
ROAD AREA	179787.31	32.299 %
ROAD WIDENING AREA	1368.00	0.245 %
TOTAL AREA	556660.5	100.00%

SCALE: 1:100'

NOTE: ALL DIMENSION'S ARE IN FEET

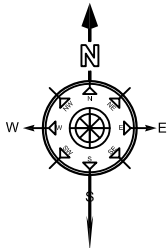

OWNER'S SIGNATURE

ARCHITECT'S SIGNATURE